
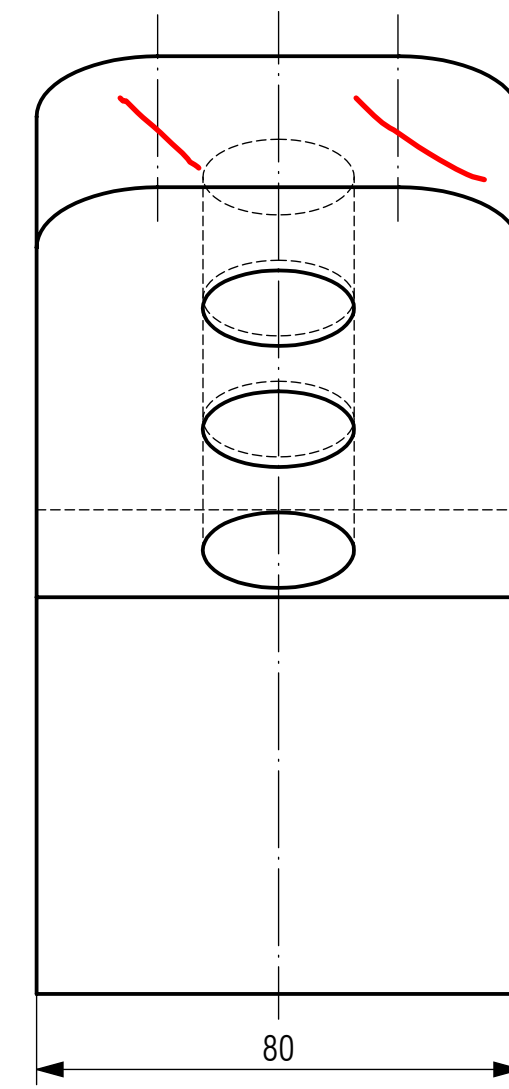


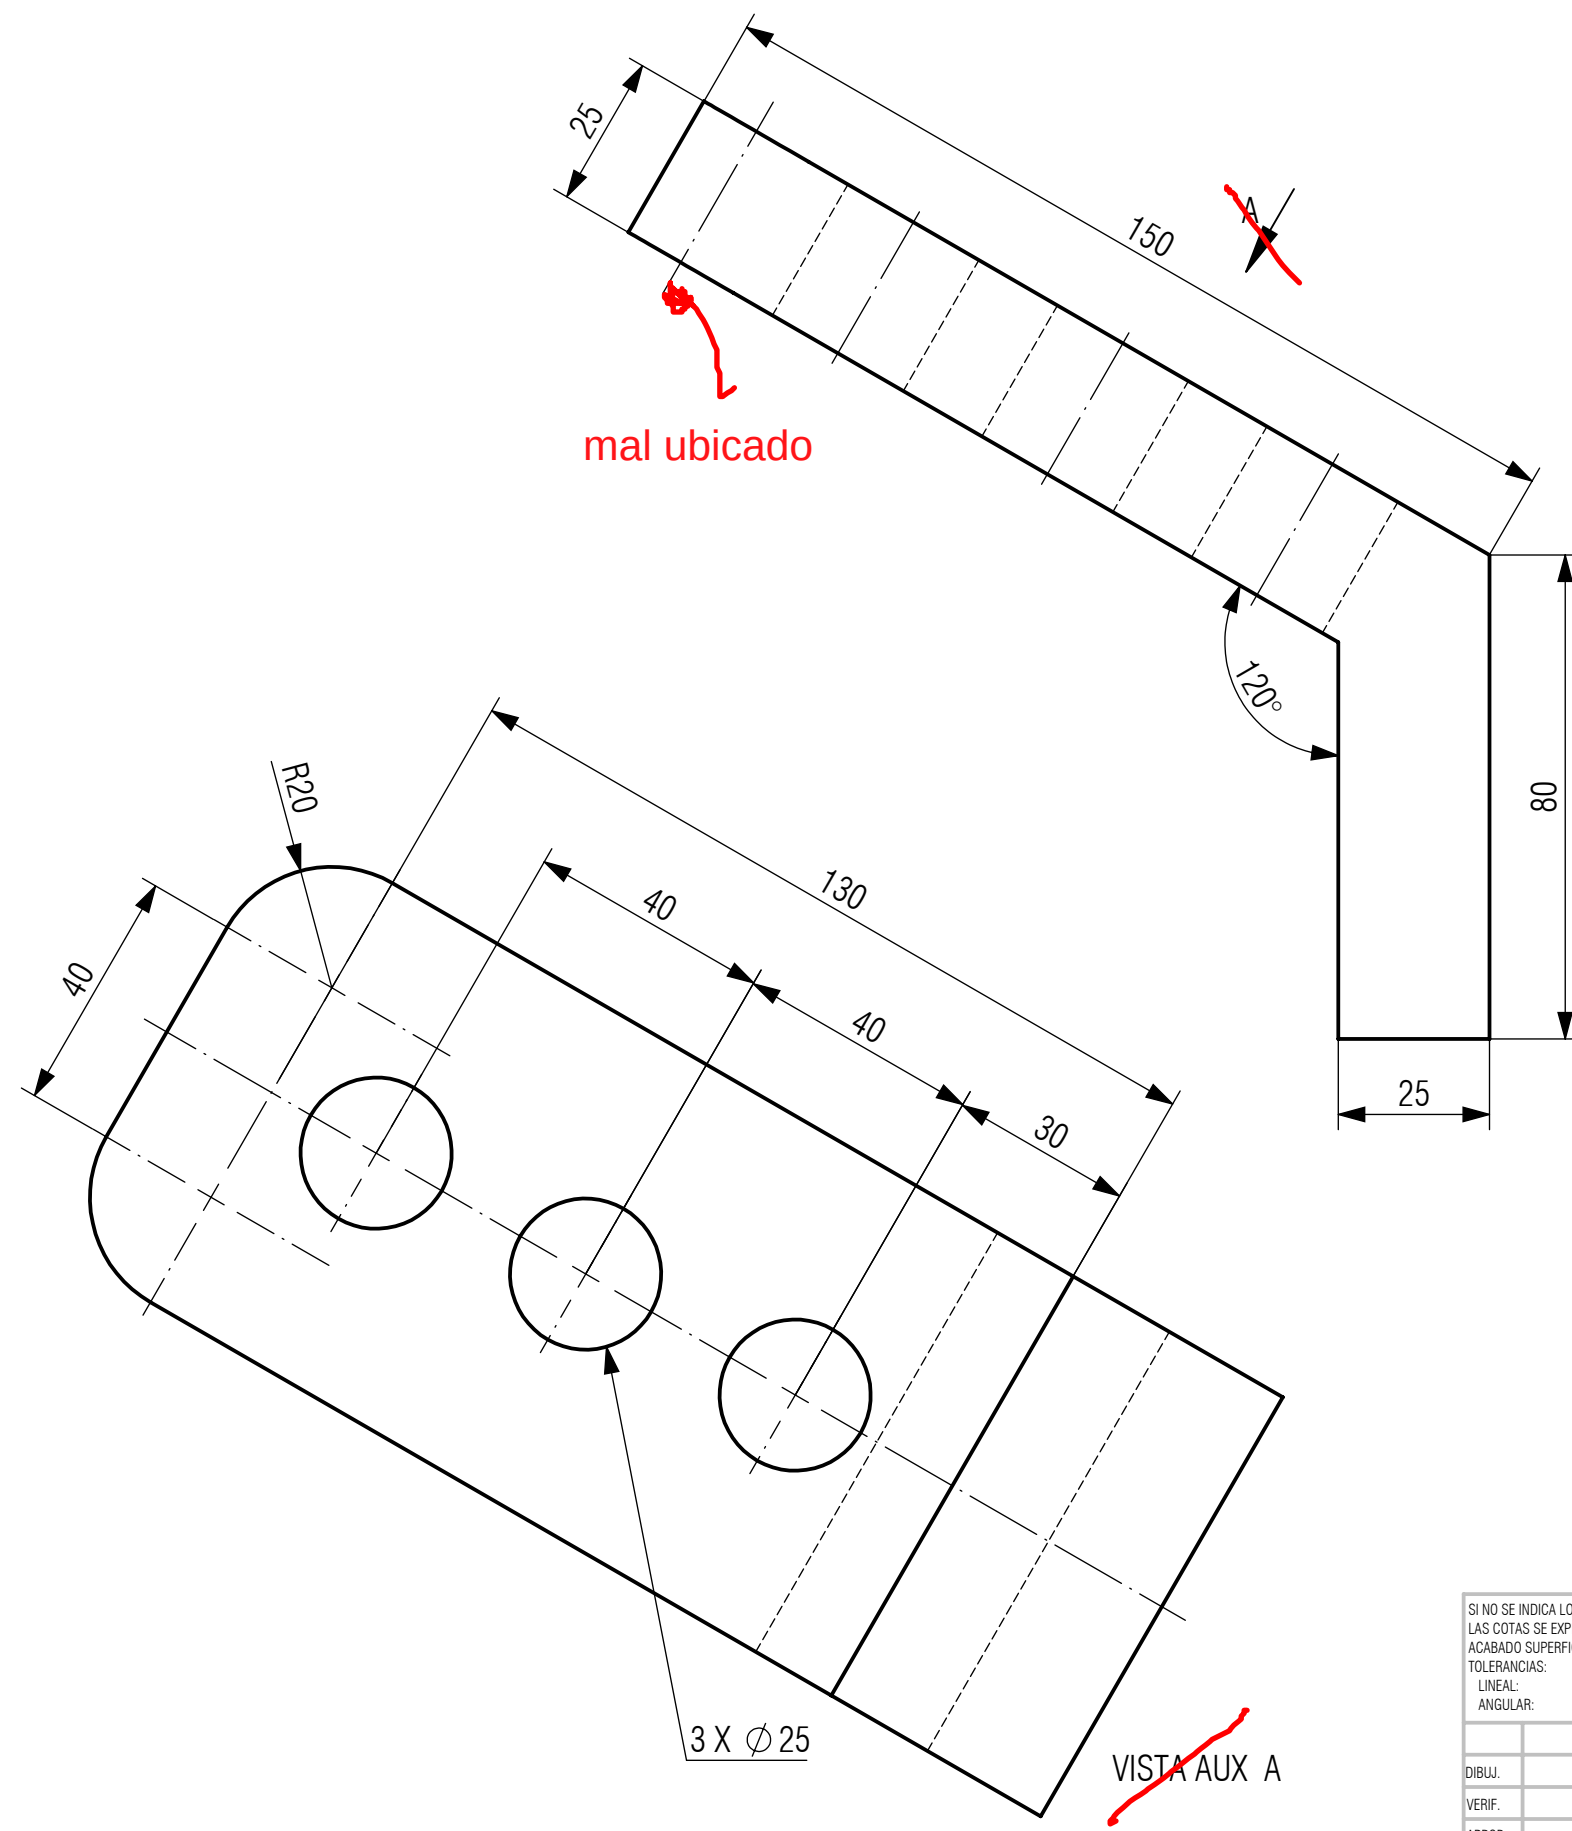

SI NO SE INDICA LO CONTRARIO: LAS COTAS SE EXPRESAN EN MM ACABADO SUPERFICIAL: TOLERANCIAS: LINEAL: ANGULAR:				ITBA		REBARBAR Y ROMPER ARISTAS VIVAS		REVISIÓN	
						SISTEMAS DE REPRESENTACION Catedra Arq. De Piero			
						TÍTULO: LÁMINA 39			
						APELLIDO Y NOMBRE K5		LEGAJO	
						ESCALA: 1:1,25		2020	
						PESO:		HOJA 1 DE 1	