
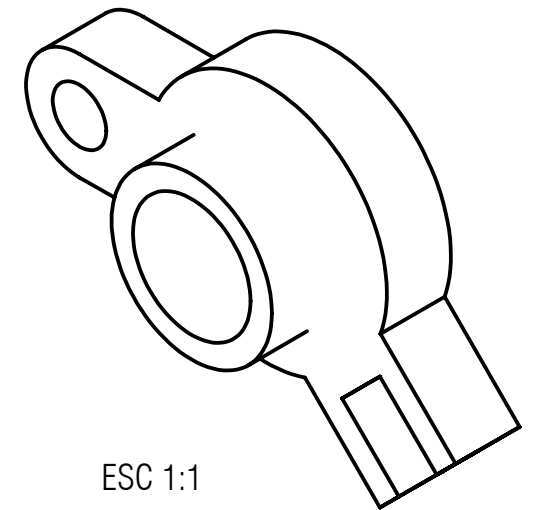
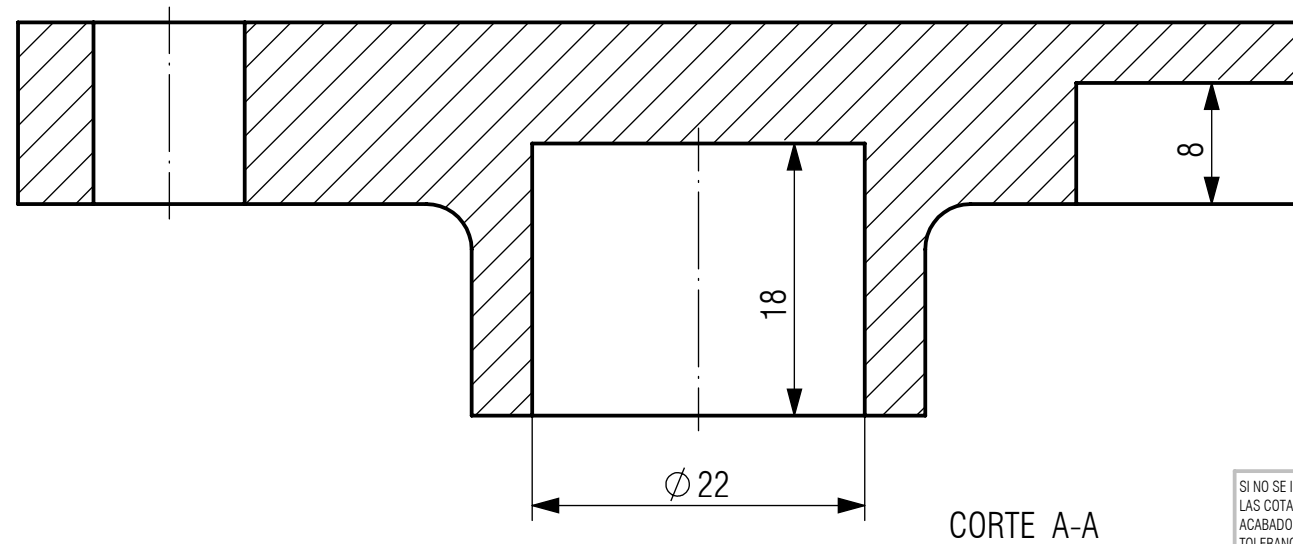
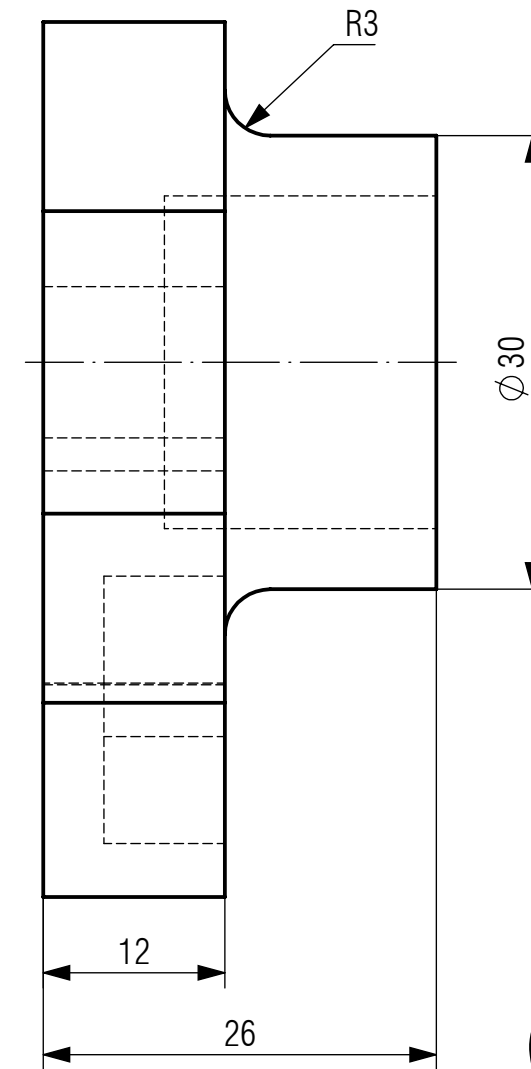


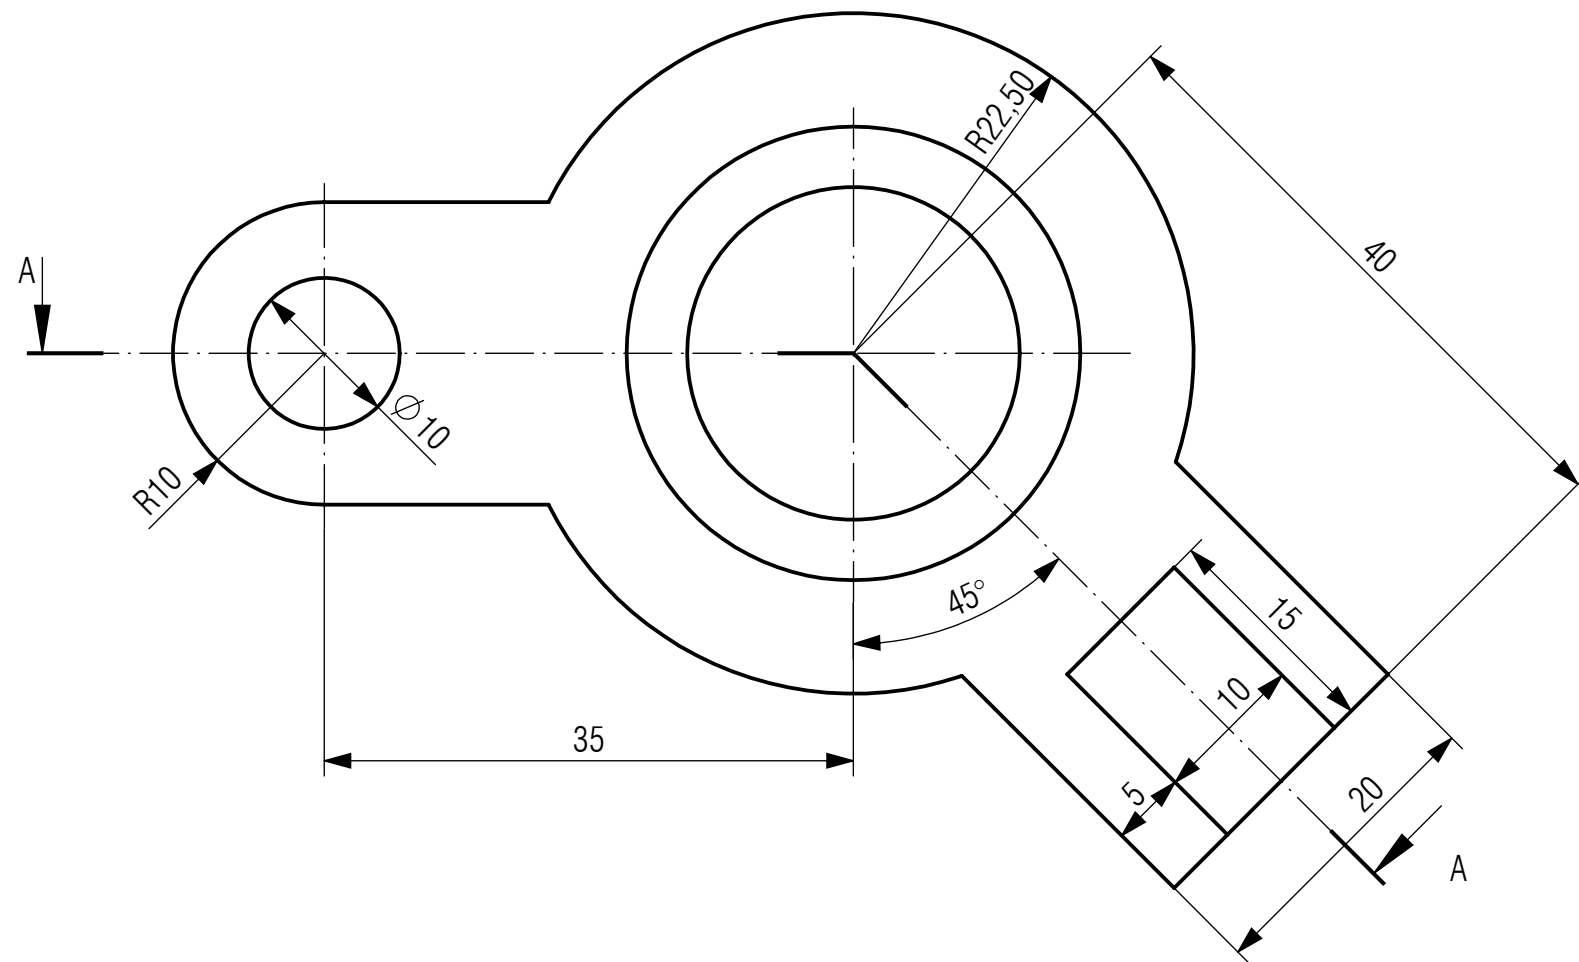

SI NO SE INDICA LO CONTRARIO: LAS COTAS SE EXPRESAN EN MM ACABADO SUPERFICIAL: TOLERANCIAS: LINEAL: ANGULAR:						REBARBAR Y ROMPER ARISTAS VIVAS	REVISIÓN
SISTEMAS DE REPRESENTACION Catedra Arq. De Piero							
TÍTULO:							
LÁMINA 5							
ESCALA: 2:1						APELLIDO Y NOMBRE K5	
PESO:						LEGAJO	2020
						HOJA 1 DE 1	